PLAN SHOWING SURVEY OF

VESTA HZ CYGNET 8-33-37-28
VESTA 103 HZ CYGNET 1-33-37-28
VESTA 102 HZ CYGNET 16-28-37-28

PAD SITE

HORIZONTALLY DRILLED FROM A SURFACE LOCATION

L.S. 5 SEC. 31 TWP. 37 RGE. 28 W.4M.

RED DEER COUNTY - ALBERTA

OPERATOR: VESTA ENERGY LTD.

AER LICENSING INFORMATION

THE PROPOSED WELL(S) :

YES	NO	
☒	☐	AT LEAST 1.5km FROM THE CORPORATE LIMITS OF AN URBAN CENTRE
☒	☐	AT LEAST 5.0km FROM ANY LIGHTED AERODROME
☒	☐	AT LEAST 1.6km FROM ANY UNLIGHTED AERODROME
☐	☒	**AT LEAST 100m FROM ANY SURFACE IMPROVEMENT** -Vesta P/L R/W
☒	☐	AT LEAST 40m FROM ANY SURVEYED ROAD
☐	☒	**AT LEAST 100m FROM THE NORMAL HIGH WATER OF ANY SIGNIFICANT BODY OF WATER** -Low Area
☒	☐	AT LEAST 200m FROM ANY WATER WELL
☒	☐	OUTSIDE ANY POTENTIAL COAL DEVELOPMENT AREA
☒	☐	OUTSIDE ANY SIGNIFICANT HISTORICAL AREA

LANDOWNER(S):

(TITLE(S) CURRENT AS OF 10/17/24)

DAVID GEORGE NINKOVICH
C. OF T. 882 295 032 A
(S.W. 31-37-28-4)


I/WE CONSENT TO THE LOCATION OF THE PAD SITE AS SHOWN AND HAVE NO OBJECTION TO THE ALBERTA ENERGY REGULATOR ISSUING A DRILLING LICENCE FOR THE SAME.

_____ _____
WITNESS



ELEVATIONS:

DATUM: CGVD28 (HTv2.0) ELEV. 938.557

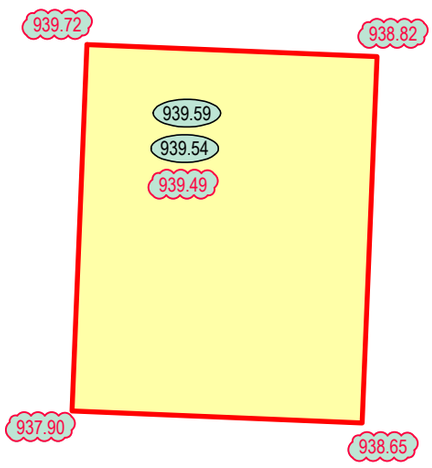

AREA(S):

	ha	Ac.
WELL SITE:	5.565	13.75

CROSSING(S):

X1 EQUS - O/H Powerline S.W.31

I, JORDAN K. WESTERA, ALBERTA LAND SURVEYOR, OF THE CITY OF RED DEER, ALBERTA, CERTIFY THAT THE SURVEY REPRESENTED BY THIS PLAN IS TRUE AND CORRECT TO THE BEST OF MY KNOWLEDGE, HAS BEEN CARRIED OUT IN ACCORDANCE WITH THE ALBERTA LAND SURVEYORS' ASSOCIATION MANUAL OF STANDARD PRACTICE, AND THE FIELD SURVEY WAS PERFORMED ON AUGUST 27th, 2024.

JORDAN K. WESTERA, ALS
DATE SIGNED: (10/21/24)

CHERYL-PATRICIA QUARTLY
(A COMMISSIONER FOR OATHS IN AND FOR ALBERTA,
COMMISSION EXPIRES ON APRIL 9, 2025)

ALBERTA LAND SURVEYORS' ASSOCIATION
PERMIT NUMBER
P266
Compass Geomatics Ltd.

COMPASS Geomatics Ltd.
11-4608 62nd Street
Red Deer, Alberta T4N 6T3
Office (403) 356-0111 Fax (403) 356-0114
www.compassgeomatics.ca

COMPASS DWG: 01148-24-PAD-R2 SURVEYED BY: VH

FINAL REVISION SUMMARY


2	ADDED DRILLS (10/21/24) JRM/MJC
1	ADDED POWERLINE PROFILE (10/08/24) JRM/MJC
0	ORIGINAL ISSUE (10/04/24) JRM/MJC

CE 941

CLIENT FILE NO. : _____
AFE NO. : _____

REV. 2

VESTA PAD SITE 5-31-37-28

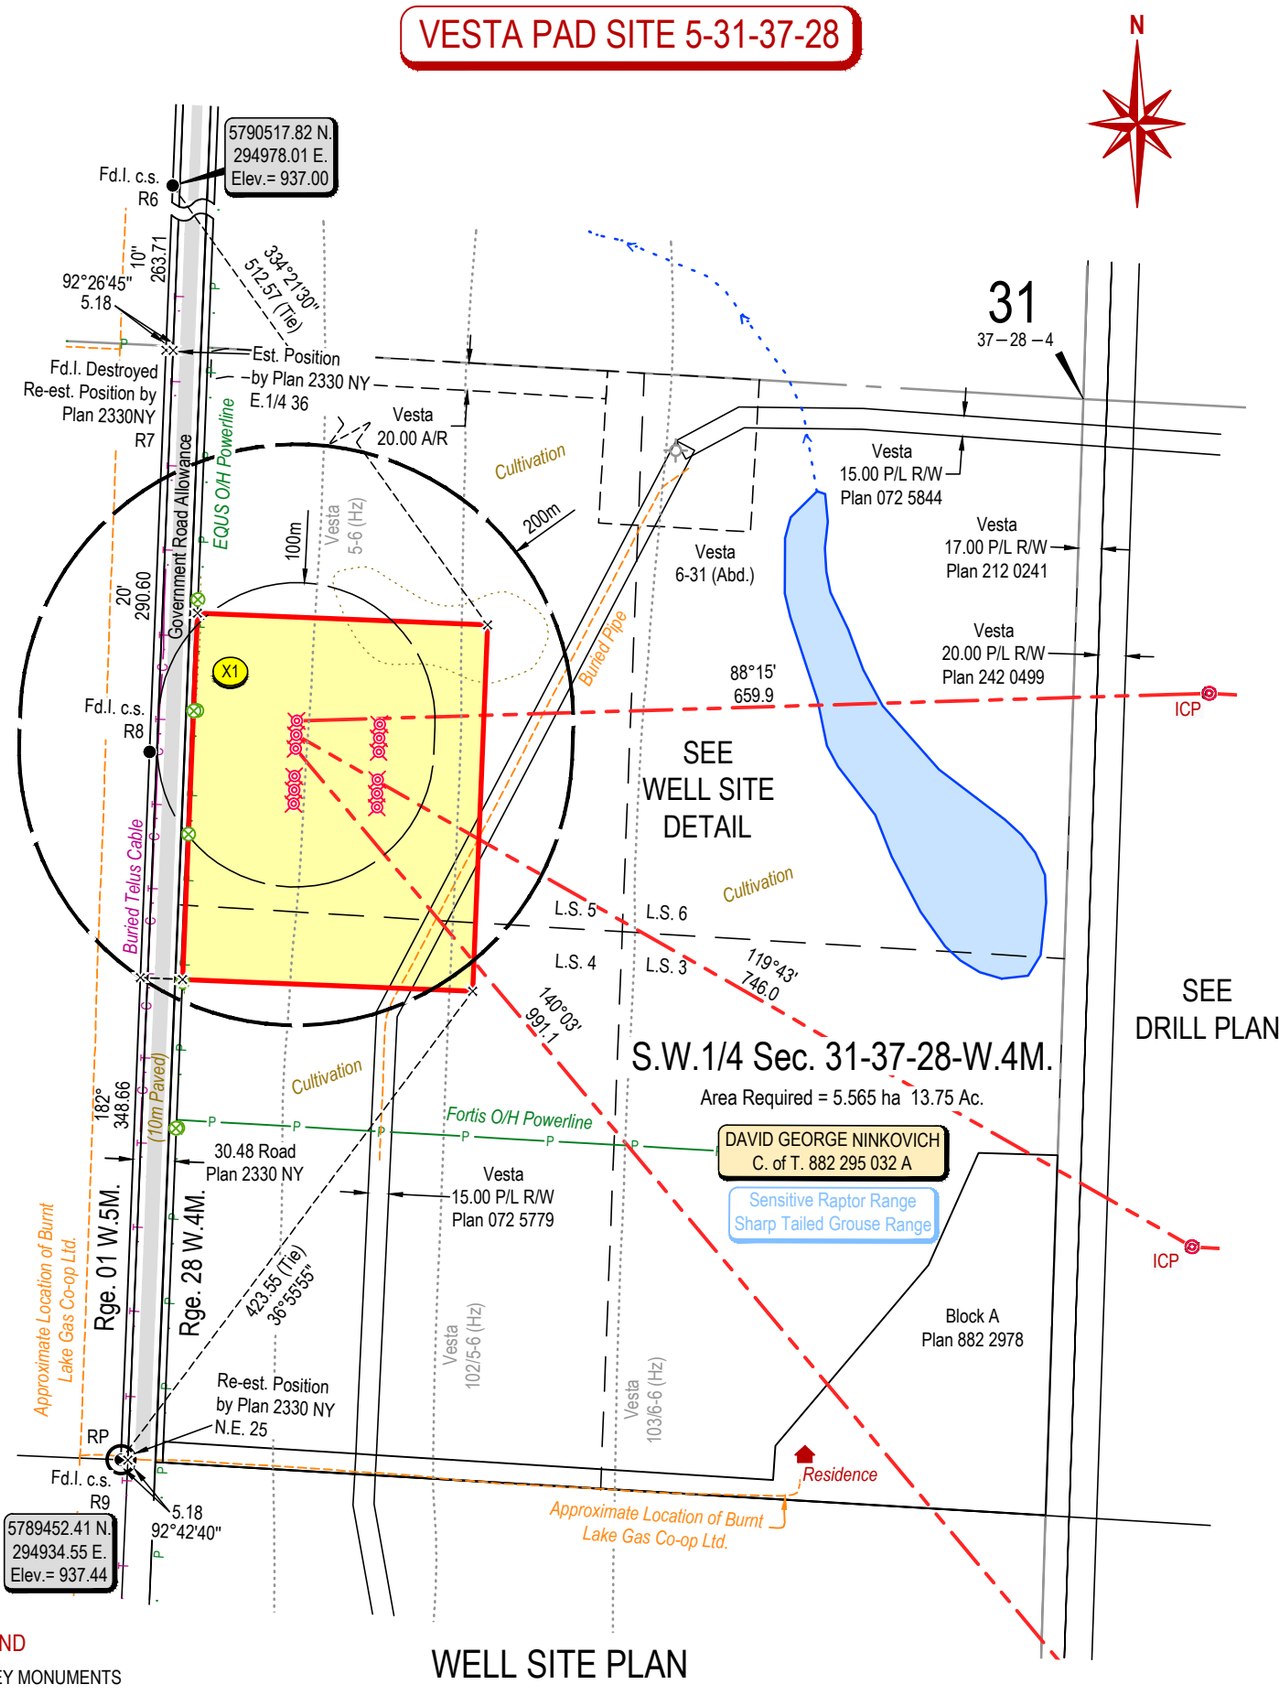

WELL SITE PLAN

SCALE 1:5000

LEGEND


SURVEY MONUMENTS
FOUND ●
30cm IRON SPIKE
FOUND ▲
PLANTED △
TEMPORARY GNSS POSITION ×
GEO-REFERENCE POINT RP ○
ELEVATIONS:
ACTUAL SHOWN THUS: 000.0
AWAITING FIELD PLACEMENT SHOWN THUS: 000.0
VEGETATION CHANGE .....
MAJOR CONTOUR INTERVAL = 2.0m
MINOR CONTOUR INTERVAL = 0.4m
PORTIONS REFERRED TO ARE SHOWN THUS:
TEMPORARY AREAS SHOWN THUS:

NOTES

BEARINGS ARE UTM NAD83 (CSRS EPOCH 2002) ZONE 12; DERIVED FROM GNSS OBSERVATIONS AND PROCESSED THROUGH PPP.
GEO-REFERENCE POINT COORDINATE IS 5789452.41 N. 294934.55 E.
COMBINED SCALE FACTOR IS 0.999972
TO CONVERT UTM GRID BEARINGS TO LOCAL ASTRONOMIC BEARINGS REFERRED TO THE CENTRAL MERIDIAN OF TWP.37 RGE.28 W.4M. SUBTRACT 2°19'10"
ASTRONOMIC BEARINGS SHOWN THUS (0°00')
DISTANCES ARE IN METRES AND DECIMALS.
LAND SEARCH CURRENT AS OF 10/15/24

SURROUNDING W/H'S AND B/H'S ARE DERIVED FROM IHS/AER/DRILLING LOGS (GRAPHIC) DATA AND SURROUNDING WELL DRILL PATHS SHOWN ARE REPRESENTATION ONLY AND ARE NOT NECESSARILY INDICATIVE OF THE TRUE ALIGNMENT.

VESTA PAD SITE 5-31-37-28

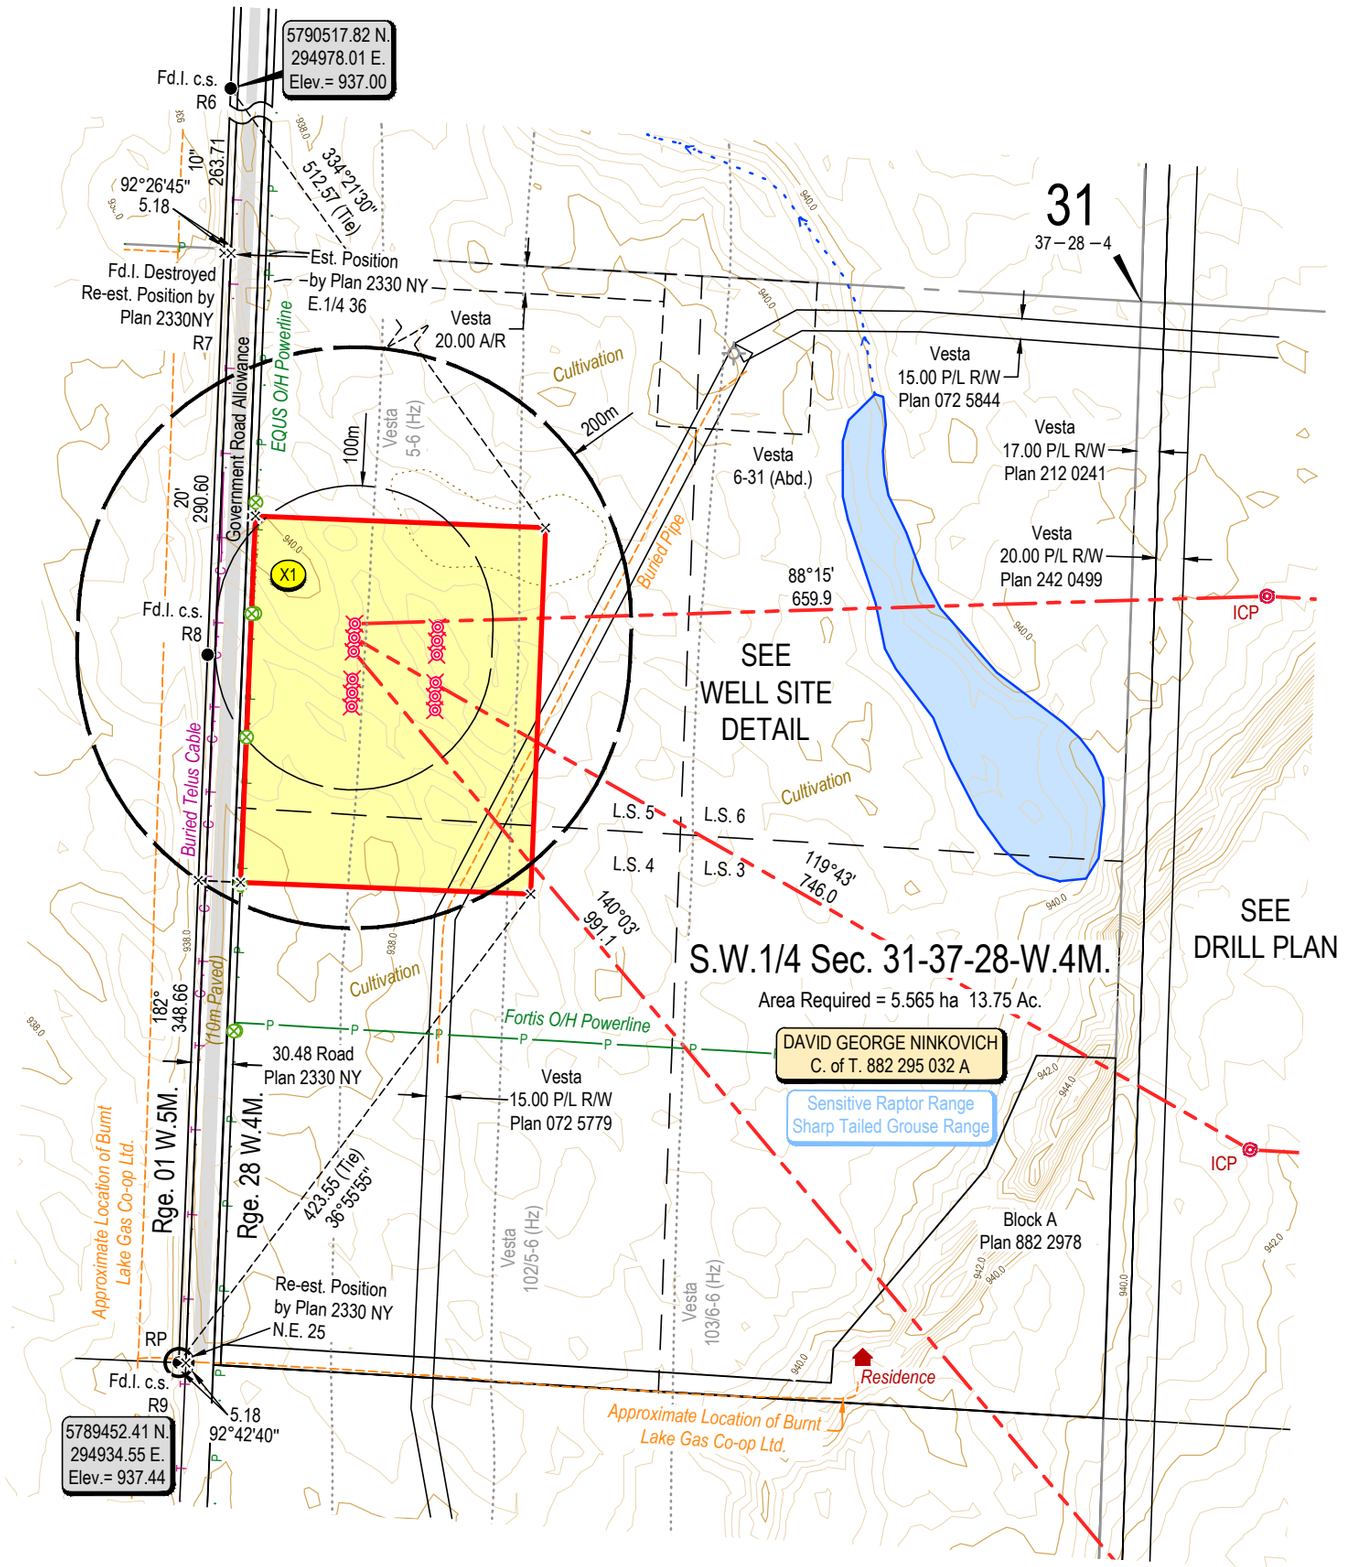


WELL SITE PLAN
WITH CONTOURS

SCALE 1:5000

MAJOR CONTOUR INTERVAL = 2.0m
MINOR CONTOUR INTERVAL = 0.4m


VESTA PAD SITE 5-31-37-28

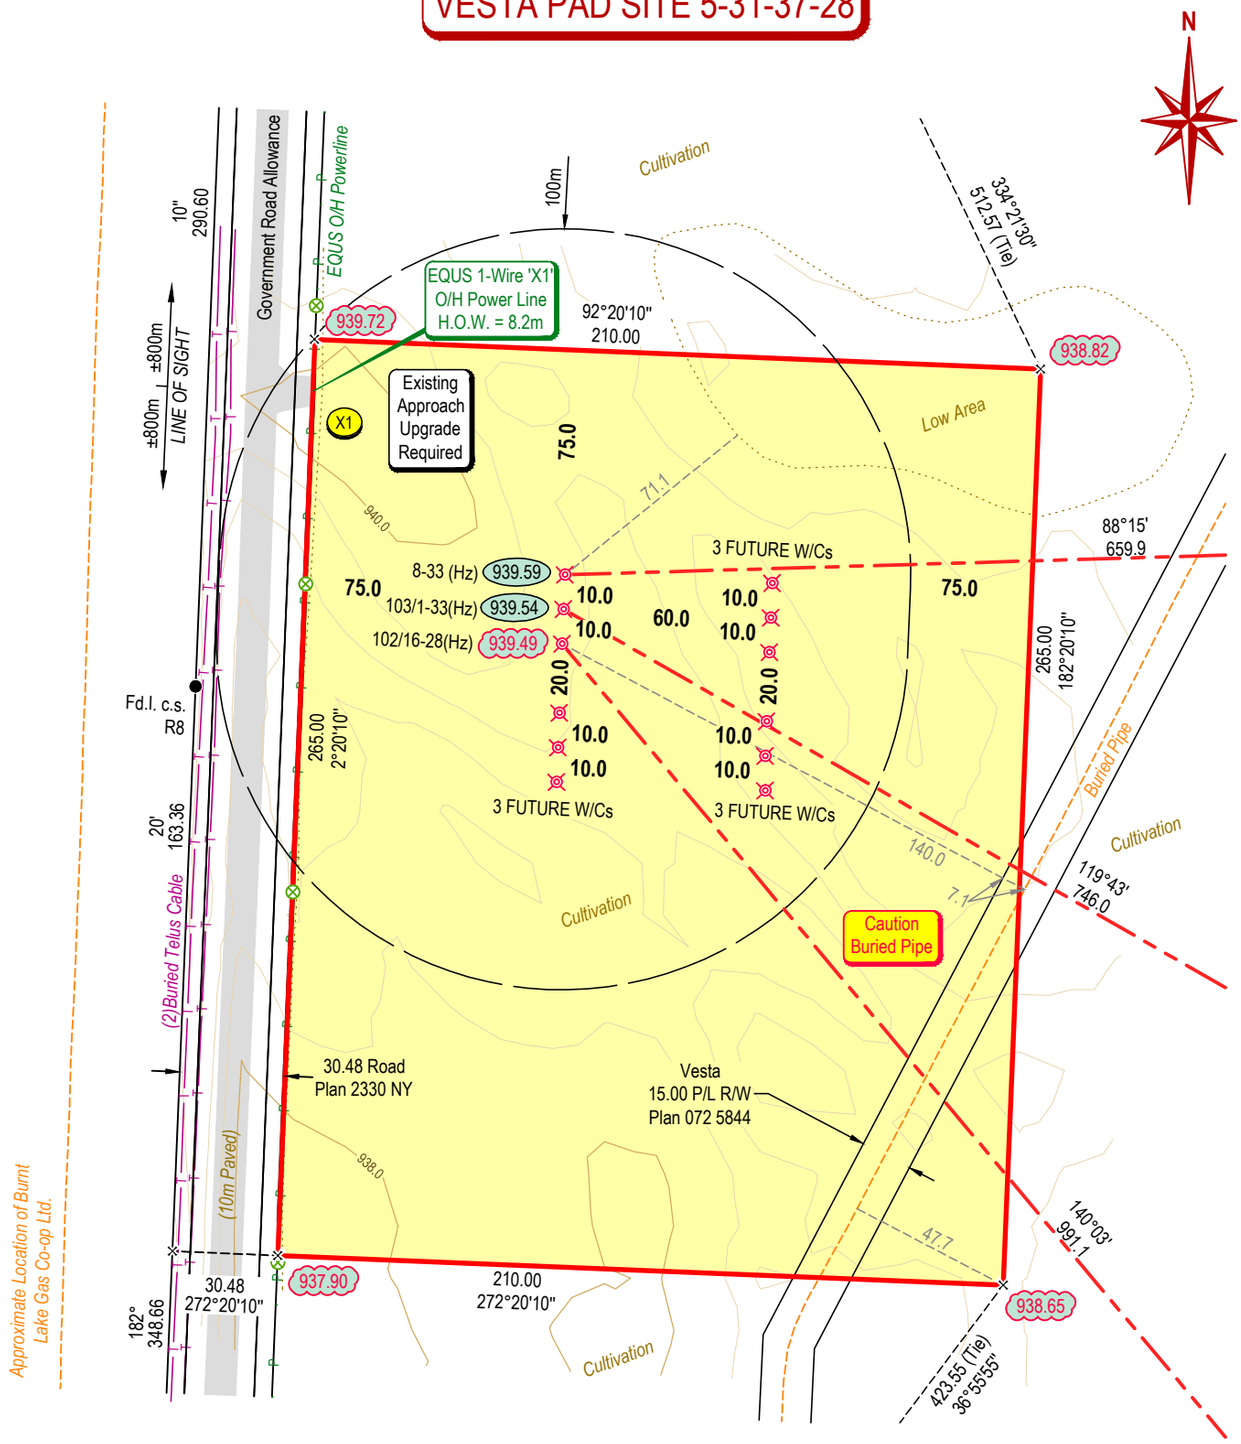

MAJOR CONTOUR INTERVAL = 2.0m
MINOR CONTOUR INTERVAL = 0.4m

WELL SITE DETAIL

SCALE 1:2000

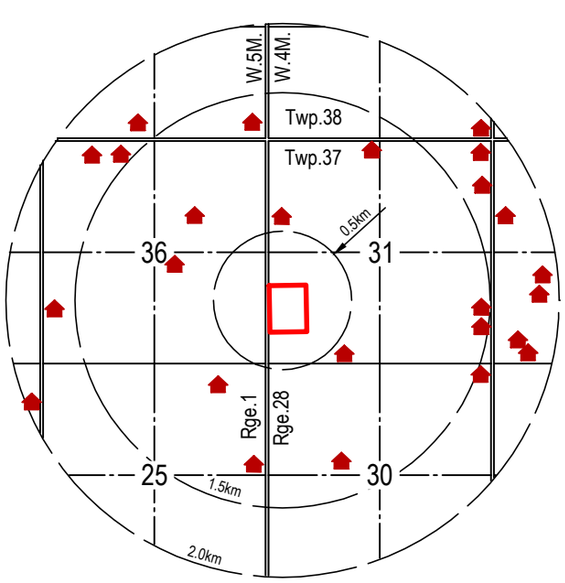

SURFACE DEVELOPMENT SKETCH


SCALE 1:50000

OCCUPIED ⌂ UNOCCUPIED ⌂ OTHER ■

WATER WELL W1 COAL MINE

NEAREST RESIDENCE
±0.63 km S.E. (S.W. 31-37-28-4)
NEAREST SURFACE DEVELOPMENT
±0.63 km S.E. (RESIDENCE, S.W. 31-37-28-4)
NEAREST URBAN CENTRE
±10.13 km S.E. (HAMLET OF SPRINGBROOK)

VESTA PAD SITE 5-31-37-28

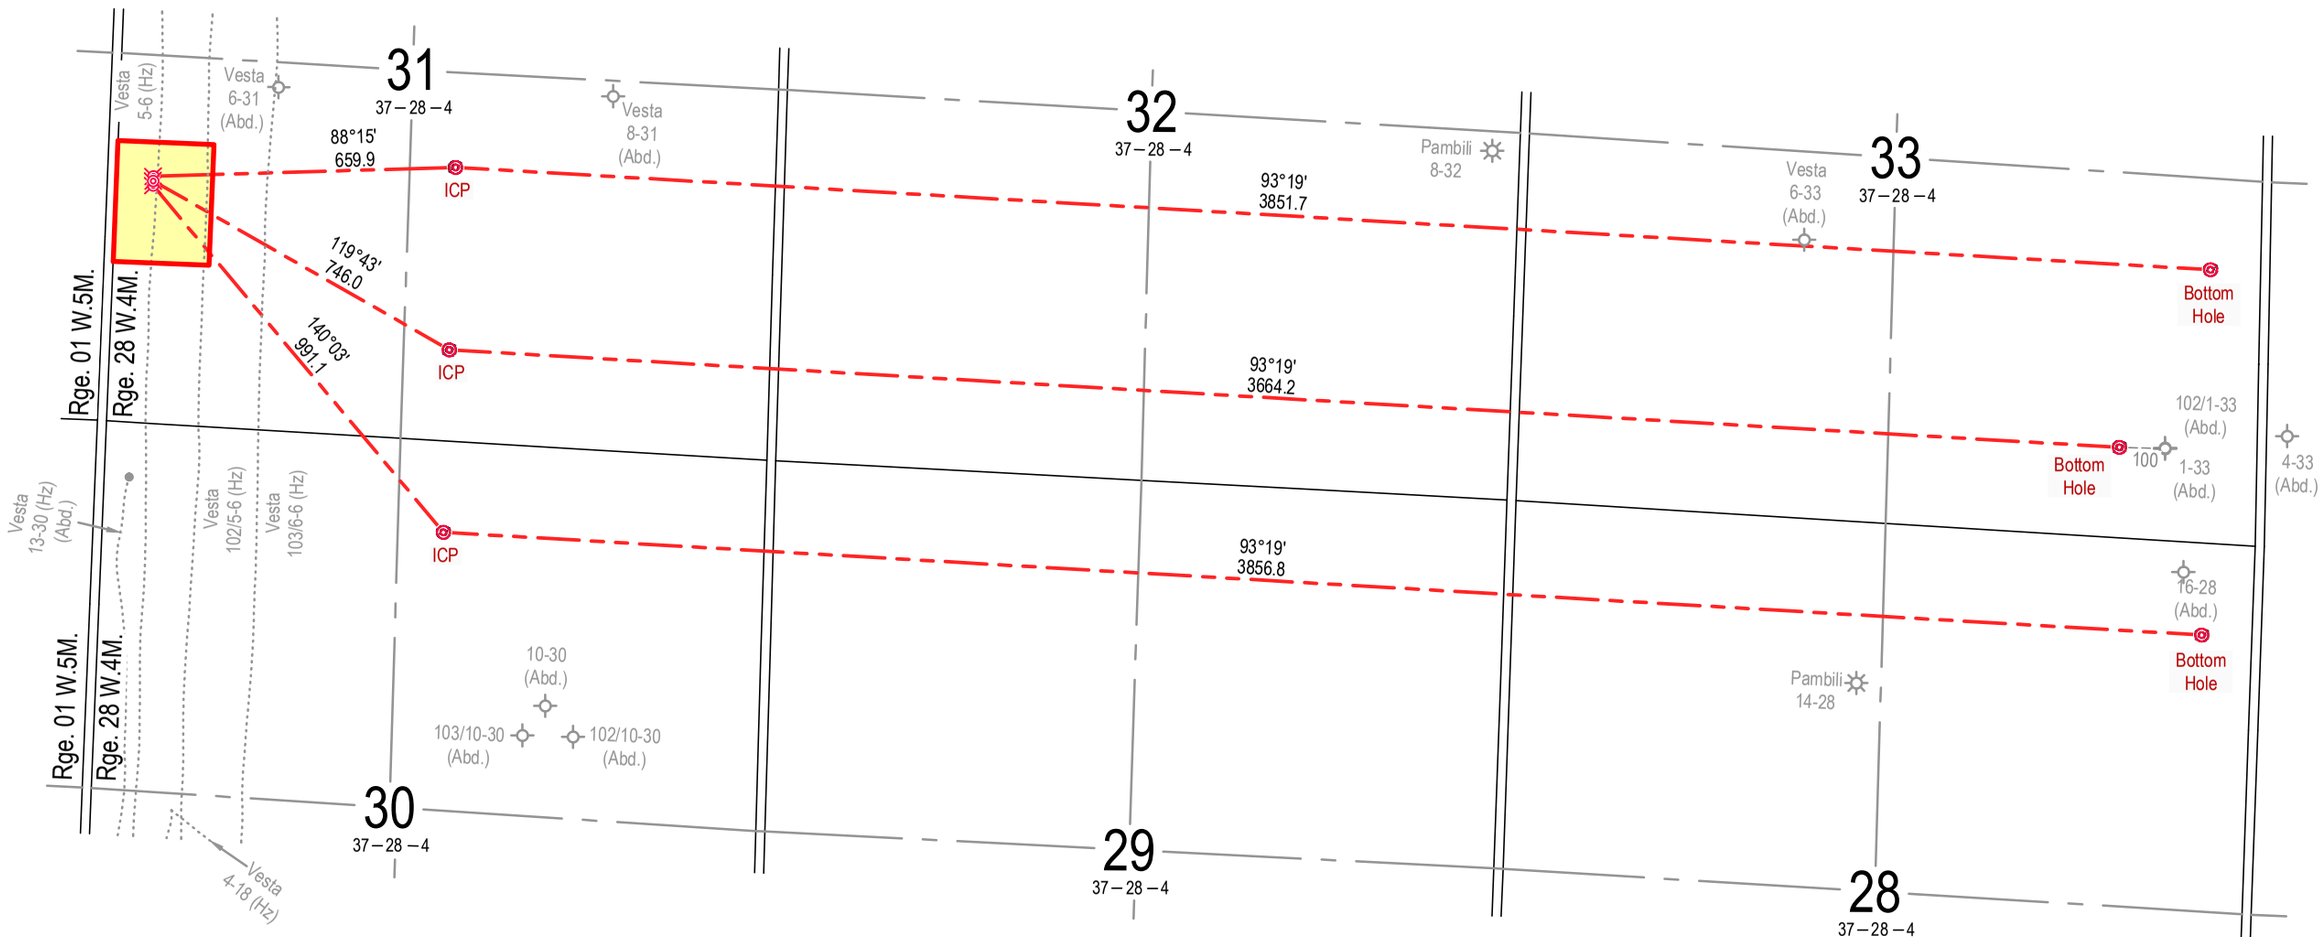

DRILL PLAN

SCALE 1:15000

DISCLAIMER THIS PLAN REPRESENTS THE BEST INFORMATION AVAILABLE AT THE TIME OF SURVEY. COMPASS GEOMATICS LTD. AND ITS EMPLOYEES TAKE NO RESPONSIBILITY FOR THE LOCATION OF ANY UNDERGROUND PIPES, CONDUITS, OR FACILITIES, WHETHER SHOWN ON OR OMITTED FROM THIS PLAN. AN ADDITIONAL SEARCH FOR SPECIFIC BURIED FACILITIES USING ALL RESOURCES MUST BE PERFORMED JUST PRIOR TO CONSTRUCTION. ALBERTA FIRST CALL 1-800-242-3447

VESTA PAD SITE 5-31-37-28

VESTA HZ CYGNET 8-33-37-28


POINT	LOCALS			UTM (NAD 83)		LAT-LONG (NAD 83)		UTM (NAD 27)		LAT-LONG (NAD 27)	
	LOCATION	METES	BOUNDS	NORTHING	EASTING	LATITUDE	LONGITUDE	NORTHING	EASTING	LATITUDE	LONGITUDE
SURFACE	05-31-037-28W4	540.5N	80.2E	5789986.31	295061.89	52.222118	-114.000449	5789759.31	295123.13	52.222061	-113.999446
ICP	07-31-037-28W4	600.03N	701.3W	5790006.04	295721.50	52.222541	-113.990818	5789779.05	295782.74	52.222484	-113.989815
BOTTOM HOLE	08-33-037-28W4	598.91N	110.0W	5789781.62	299566.56	52.221938	-113.934471	5789554.62	299627.85	52.221880	-113.933469

VESTA 103 HZ CYGNET 1-33-37-28

POINT	LOCALS			UTM (NAD 83)		LAT-LONG (NAD 83)		UTM (NAD 27)		LAT-LONG (NAD 27)	
	LOCATION	METES	BOUNDS	NORTHING	EASTING	LATITUDE	LONGITUDE	NORTHING	EASTING	LATITUDE	LONGITUDE
SURFACE	05-31-037-28W4	530.5N	80.2E	5789976.31	295061.49	52.222028	-114.000449	5789749.32	295122.72	52.221971	-113.999446
ICP	02-31-037-28W4	200.0N	702.2W	5789606.15	295709.84	52.218946	-113.990747	5789379.15	295771.10	52.218889	-113.989744
BOTTOM HOLE	01-33-037-28W4	200.0N	301.6W	5789393.66	299367.20	52.218382	-113.937155	5789166.66	299428.50	52.218324	-113.936154

VESTA 102 HZ CYGNET 16-28-37-28

POINT	LOCALS			UTM (NAD 83)		LAT-LONG (NAD 83)		UTM (NAD 27)		LAT-LONG (NAD 27)	
	LOCATION	METES	BOUNDS	NORTHING	EASTING	LATITUDE	LONGITUDE	NORTHING	EASTING	LATITUDE	LONGITUDE
SURFACE	05-31-037-28W4	520.5N	80.2E	5789966.32	295061.08	52.221939	-114.000449	5789739.33	295122.31	52.221882	-113.999446
ICP	15-30-037-28W4	200.0S	702.8W	5789206.22	295697.04	52.215350	-113.990693	5788979.22	295758.30	52.215293	-113.989690
BOTTOM HOLE	16-28-037-28W4	200.0S	110.0W	5788981.17	299547.45	52.214744	-113.934276	5788754.17	299608.75	52.214686	-113.933275

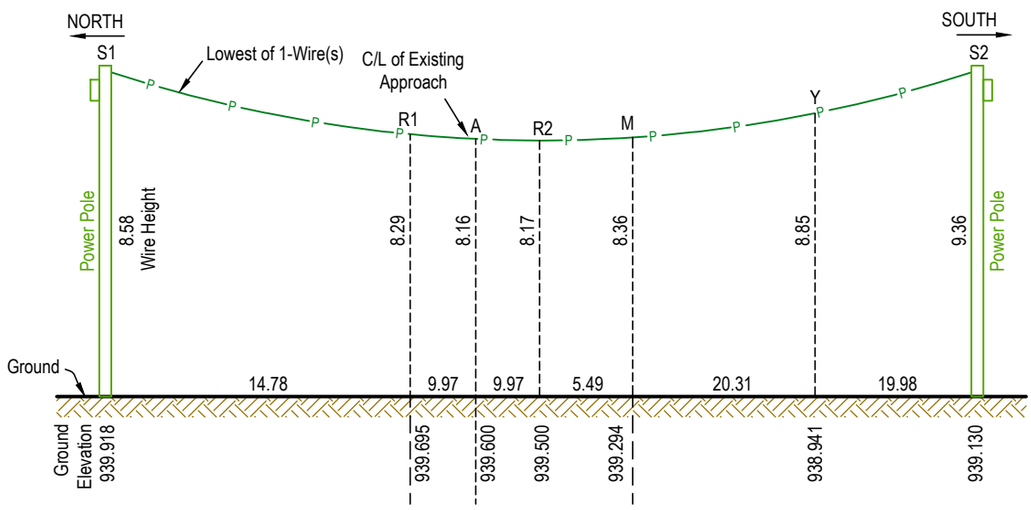


Date: August 27th, 2024

Ambient Temperature: 17°C
Weather Conditions: Overcast

POWERLINE CROSSING DETAIL

NOT TO SCALE

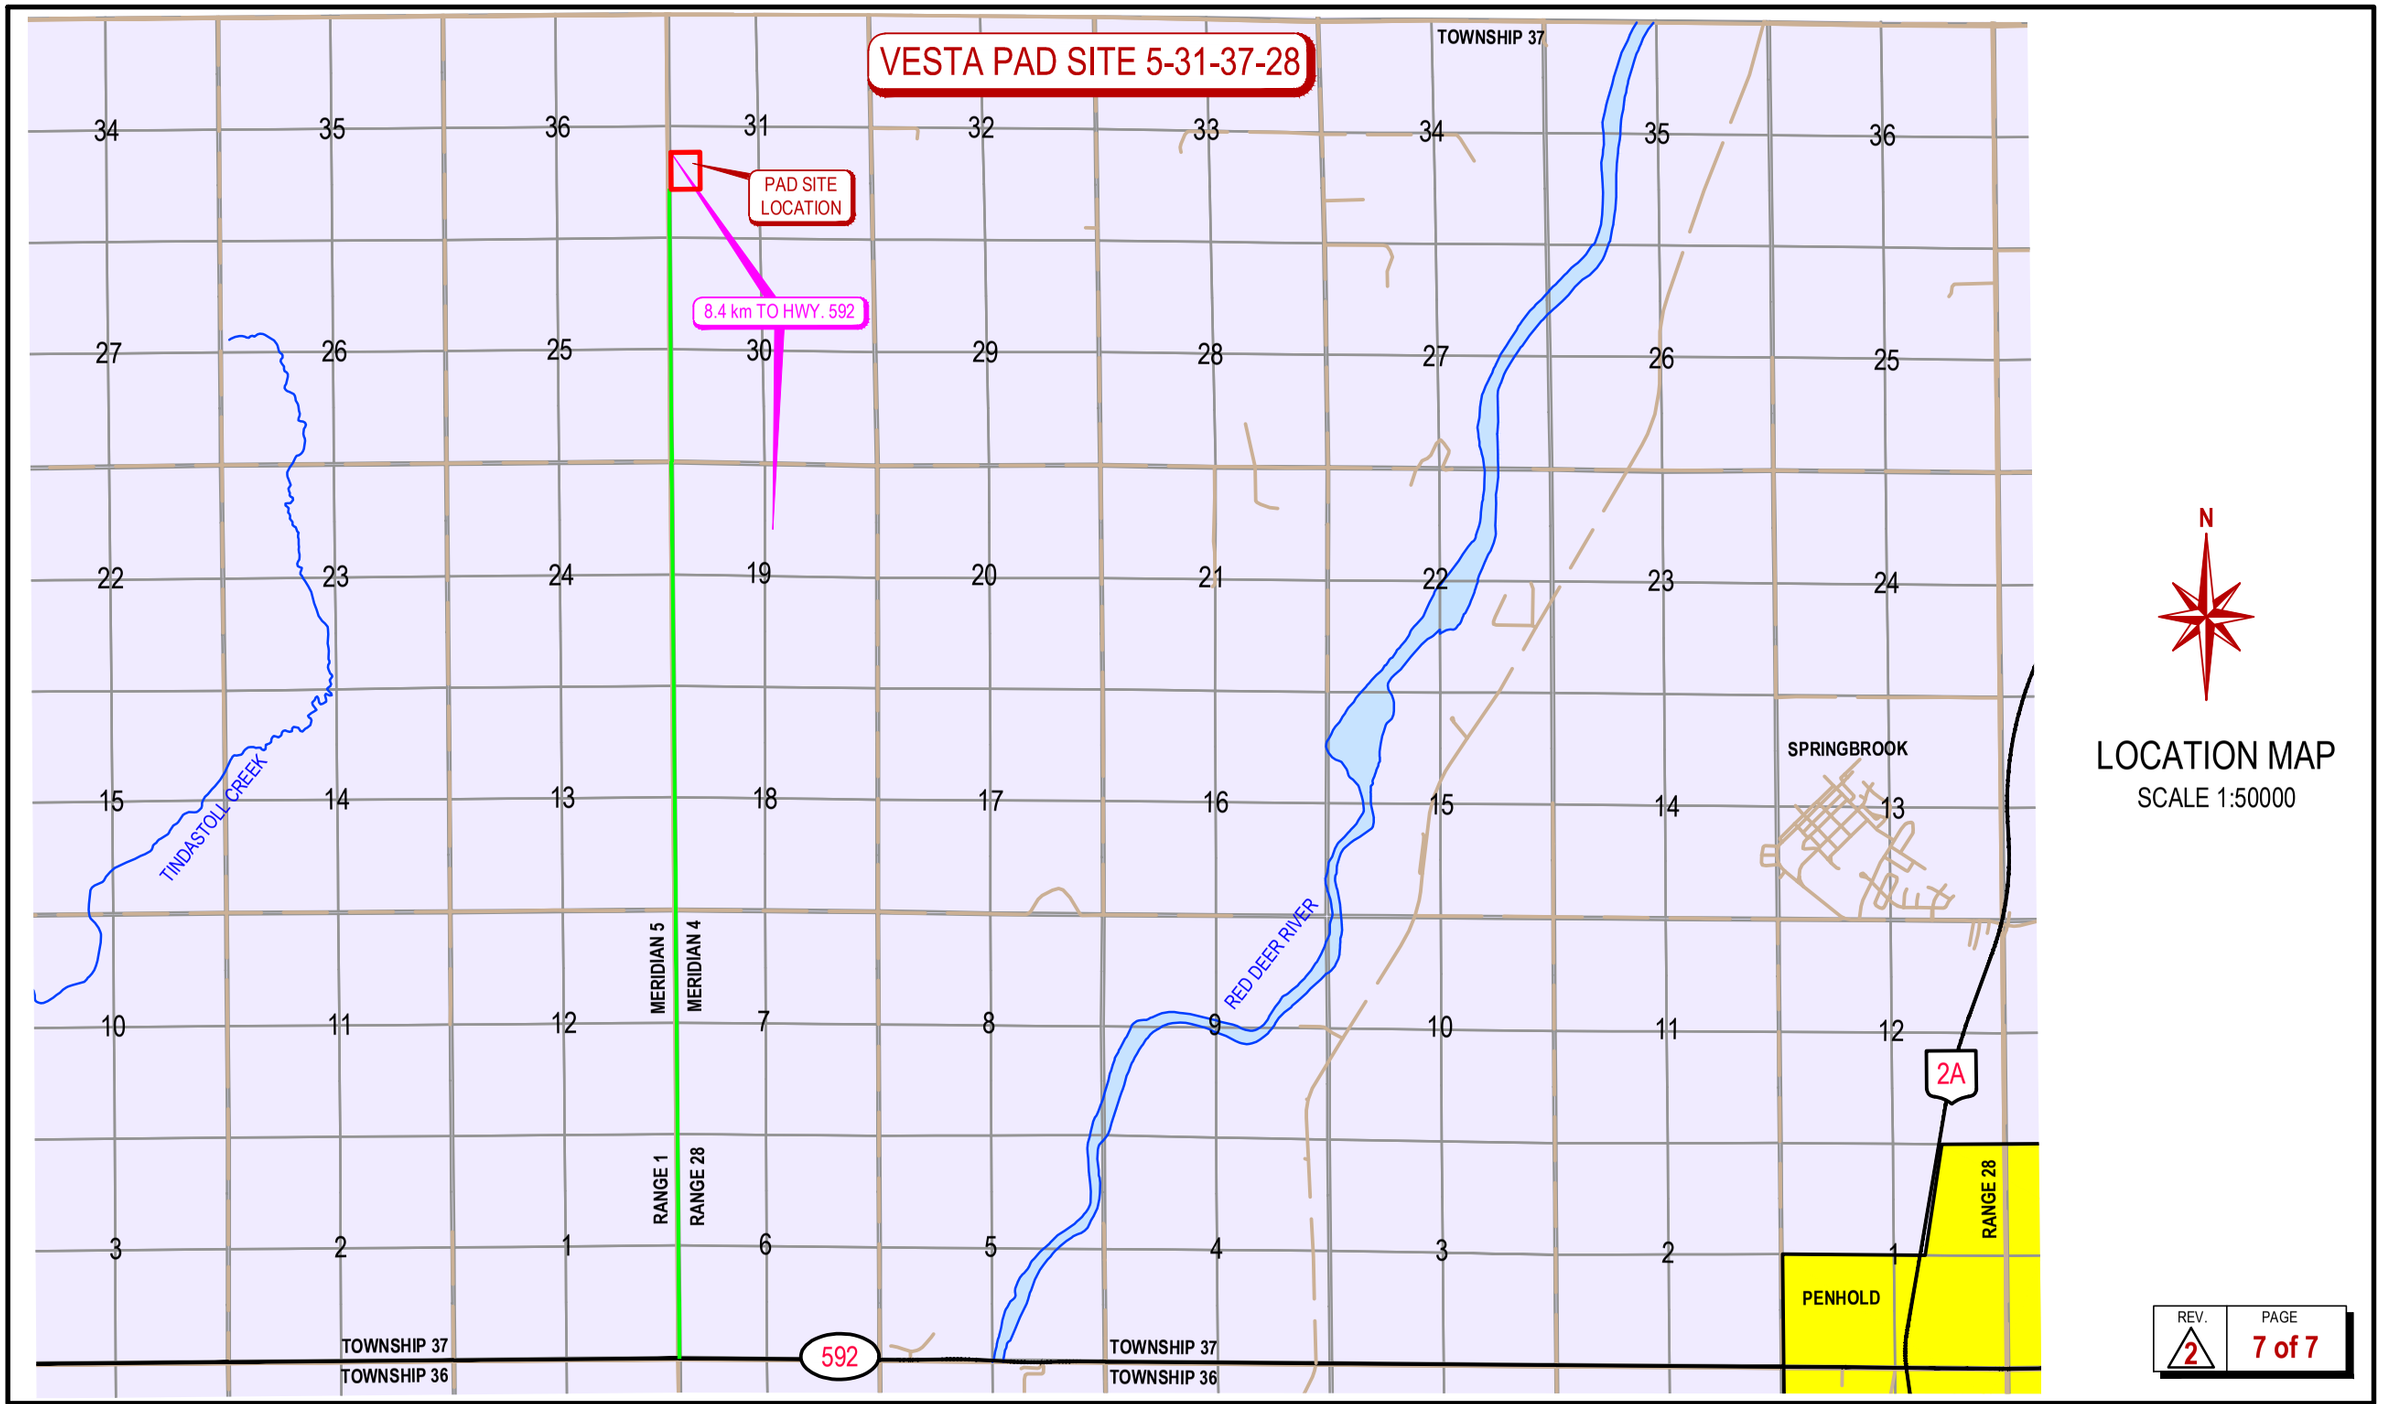


VESTA PAD SITE 5-31-37-28
PAD SITE LOCATION
8.4 km TO HWY. 592
TOWNSHIP 37
TOWNSHIP 36
TINDASTOLL CREEK
RED DEER RIVER
SPRINGBROOK
PENHOLD
MERIDIAN 5
MERIDIAN 4
RANGE 1
RANGE 28
RANGE 28
592
2A
N
LOCATION MAP
SCALE 1:50000
REV. 2
PAGE 7 of 7